




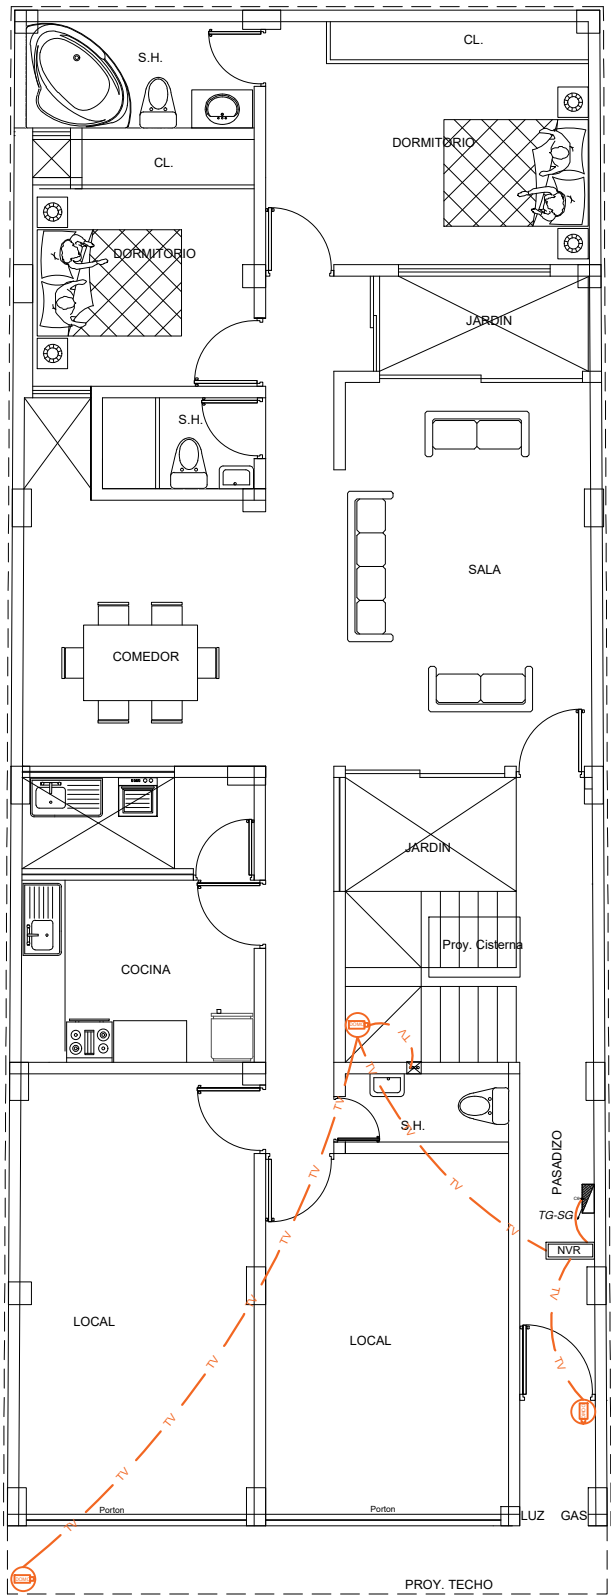



PRIMERA PLANTA

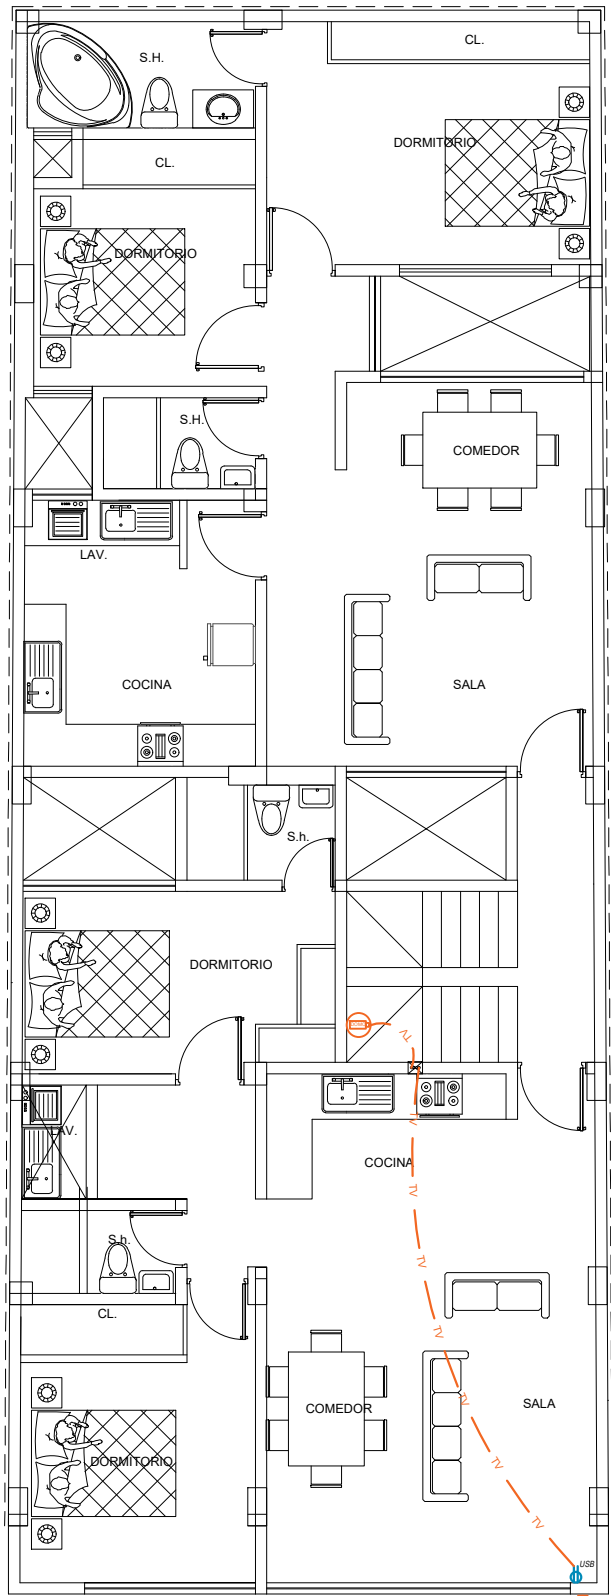

2°, 3° Y 4° PLANTA

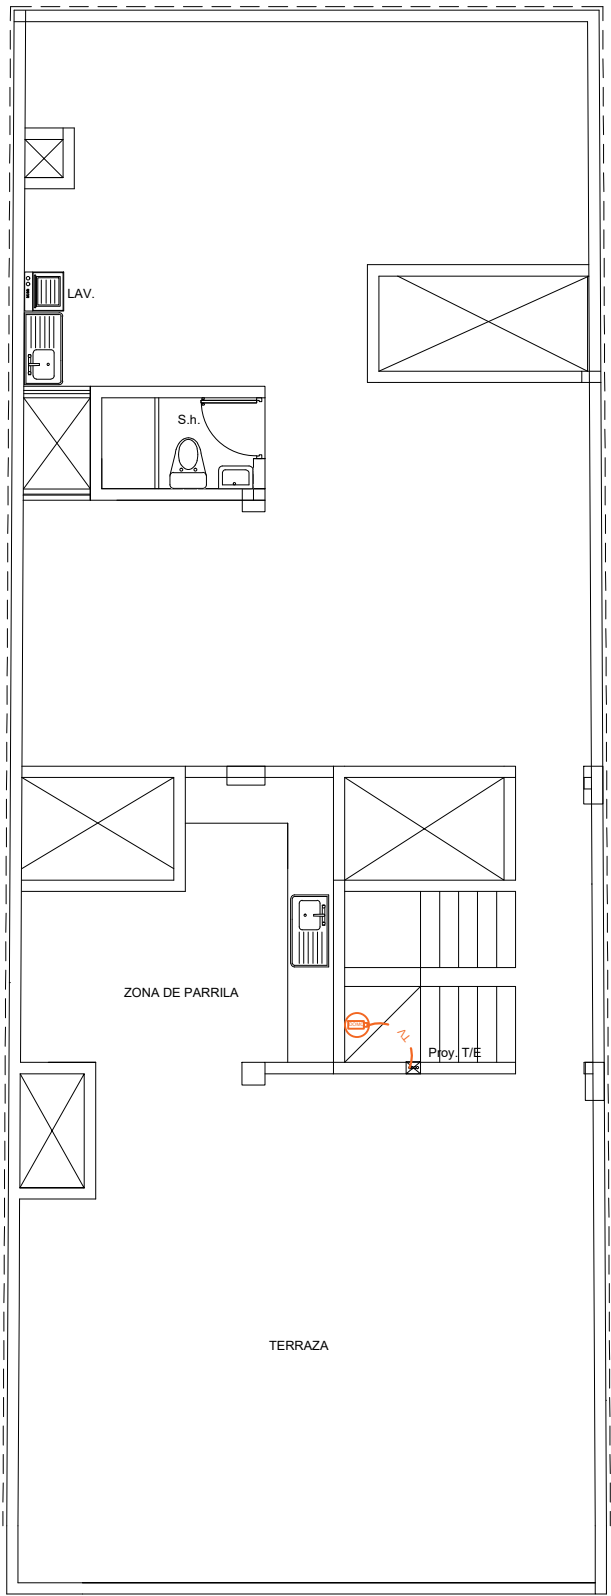

PLANTA AZOTEA

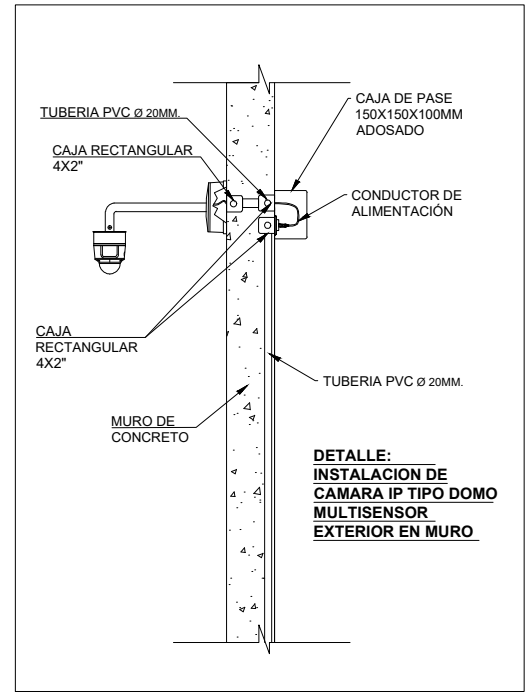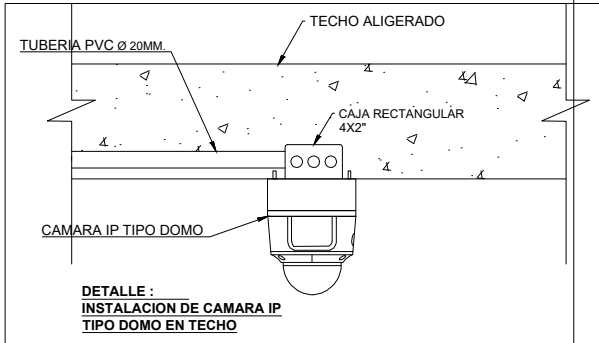

NOTA:

- Las cámaras de seguridad son recargables con sensor de movimiento y comunicación Wifi.
- Los puntos exteriores e interiores de las camaras de vigilancia deben ser resguardados mediante cajas cuadradas de proteccion IP 66.
- Las tapas deberán adoptar el mismo color del acabado de techo y paredes.
- Las imágenes de los detalles son referenciales.

LEYENDA DEL SISTEMA DE VIDEOVIGILANCIA			
SIMBOLO	DESCRIPCION	RESOLUCION	MONTAJE (m)
	CÁMARA TIPO I DOMO P/ADOSAR CON SOPORTE EN TECHO	4MP	Techo
	CIRCUITO CERRADO DE TV	---	Empotrado
	CÁMARA TIPO DOMO MULTISENSOR CON SOPORTE METALICO	8MP	INDICADA

DALINA EPIFANÍA CHAMORRO VILLAFUERTE
VIVIENDA MULTIFAMILIAR

Especialidad:
CIRCUITO CERRADO DE VIDEO VIGILANCIA

Fecha:
ABRIL 2026

Escala:

Ubicación:
MZ F, LOTE 3
COOPERATIVA VIRGEN DE FÁTIMA, SAN MARTÍN DE PORRES, LIMA.

Lamina:
IE-07



Plano: INSTALACIONES ELÉCTRICAS

